
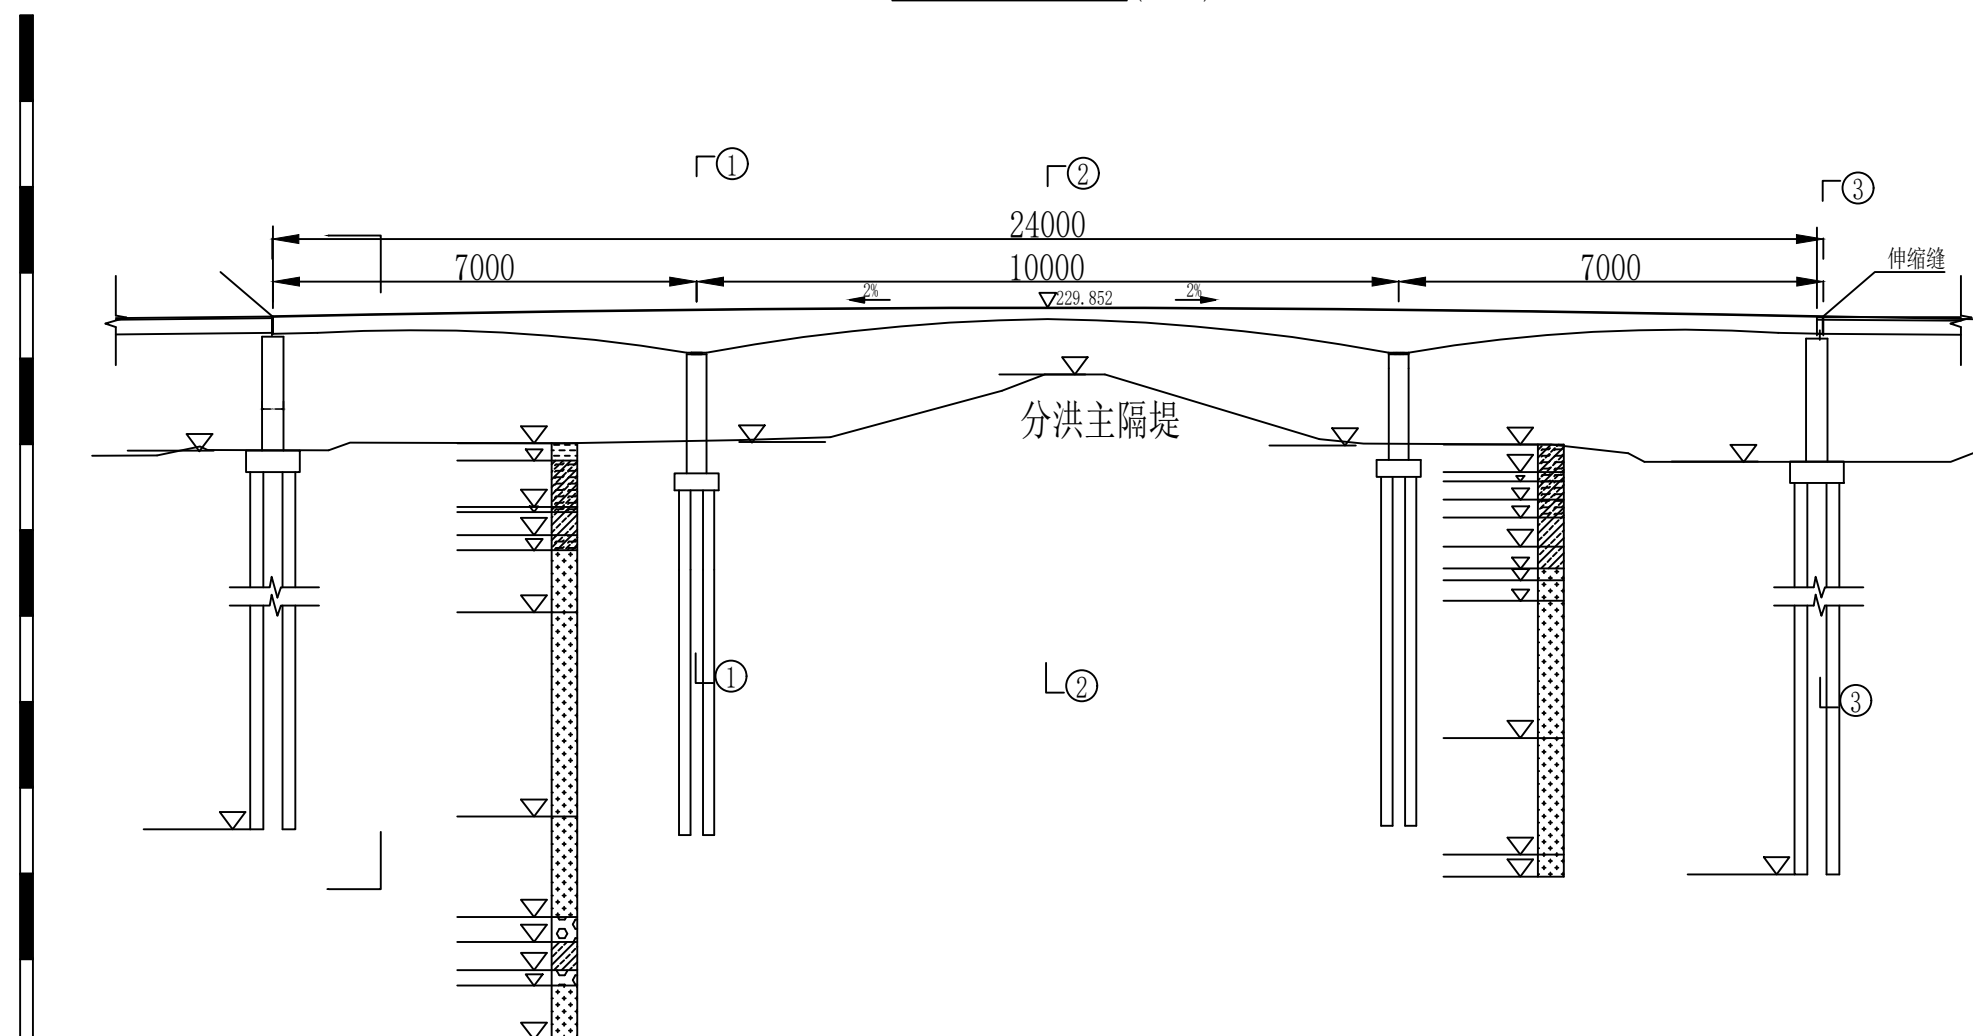
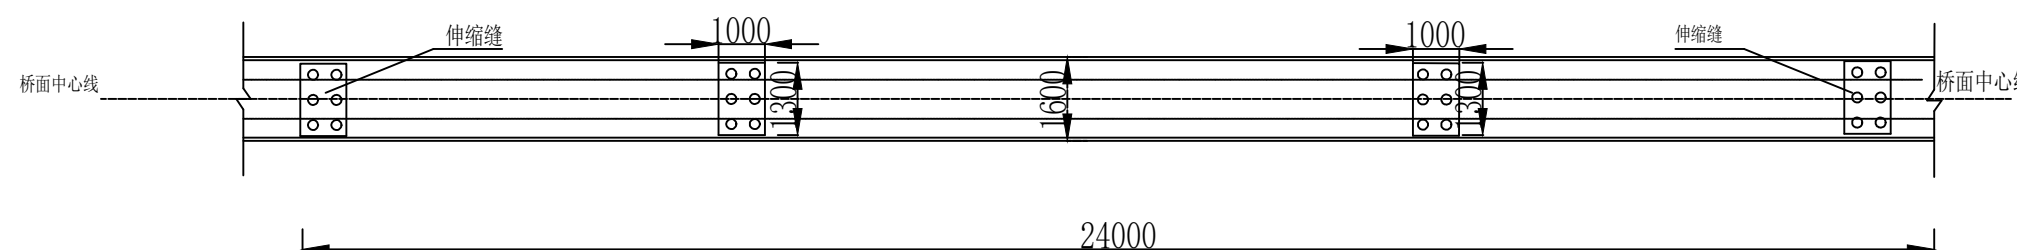
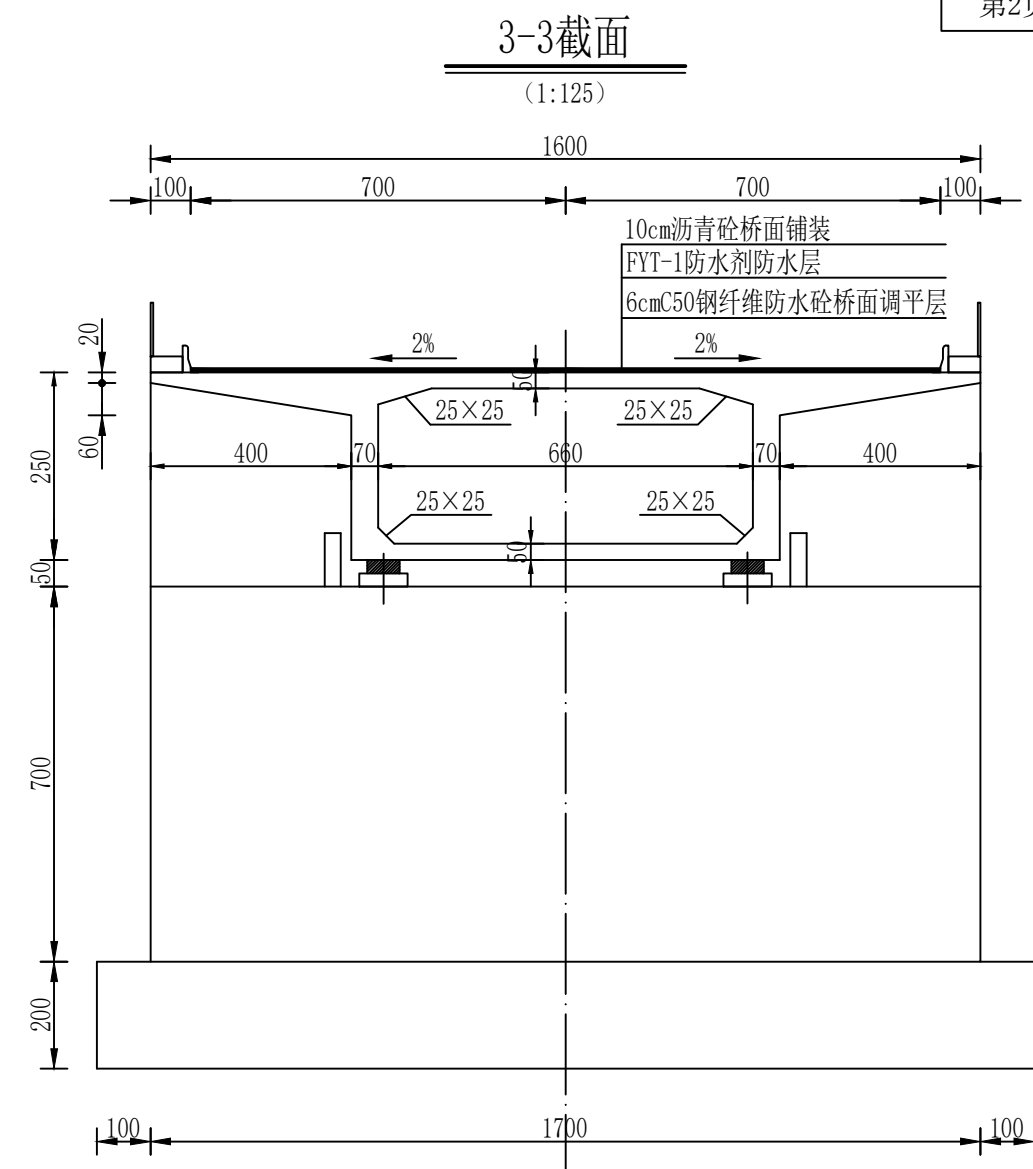


全桥桥型布置图
(1:600)全桥平面布置图
(1:1000)

- 注：
1. 本图尺寸除标高、里程桩号以m计外，余均以cm计。
 2. 本图高程均采用黄海高程系。
 3. 桥面宽度：净14m+2×1m。
 4. 设计荷载：公路-I级，人群荷载：3.0KN/m²。
 5. 通航标准：无。
 6. 地震标准：基本烈度6度，按构造设防。
 7. 平曲线：不设平曲线。
 8. 纵坡及竖曲线：i=±2%，竖曲线半径R=6000m。
 9. 桥型：70+120+70m预应力混凝土变截面连续梁桥。

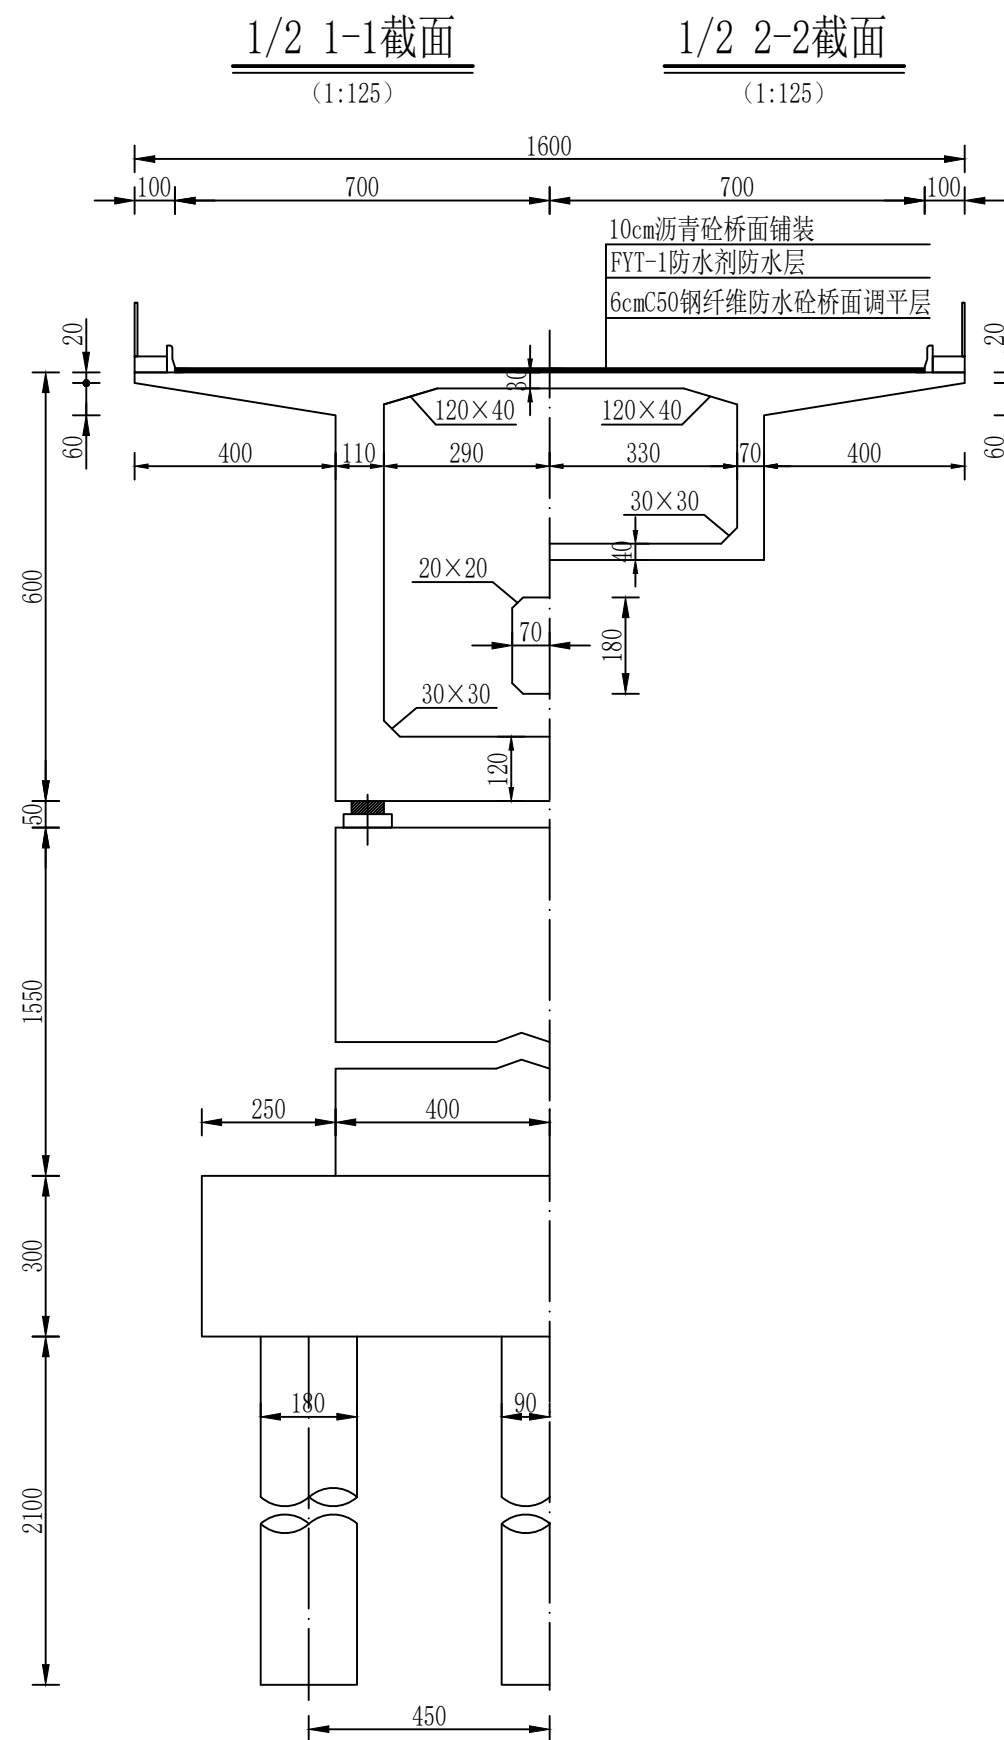

注:

1. 本图尺寸均以cm计。
2. 桥面净宽: 净14m+2×1m。
3. 桥面横坡: 行车道2%, 人行道1%。
4. 桥面铺装: 10cm厚沥青砼桥面铺装层+FYT-1防水剂防水层+6cmC50钢纤维防水砼桥面调平层。